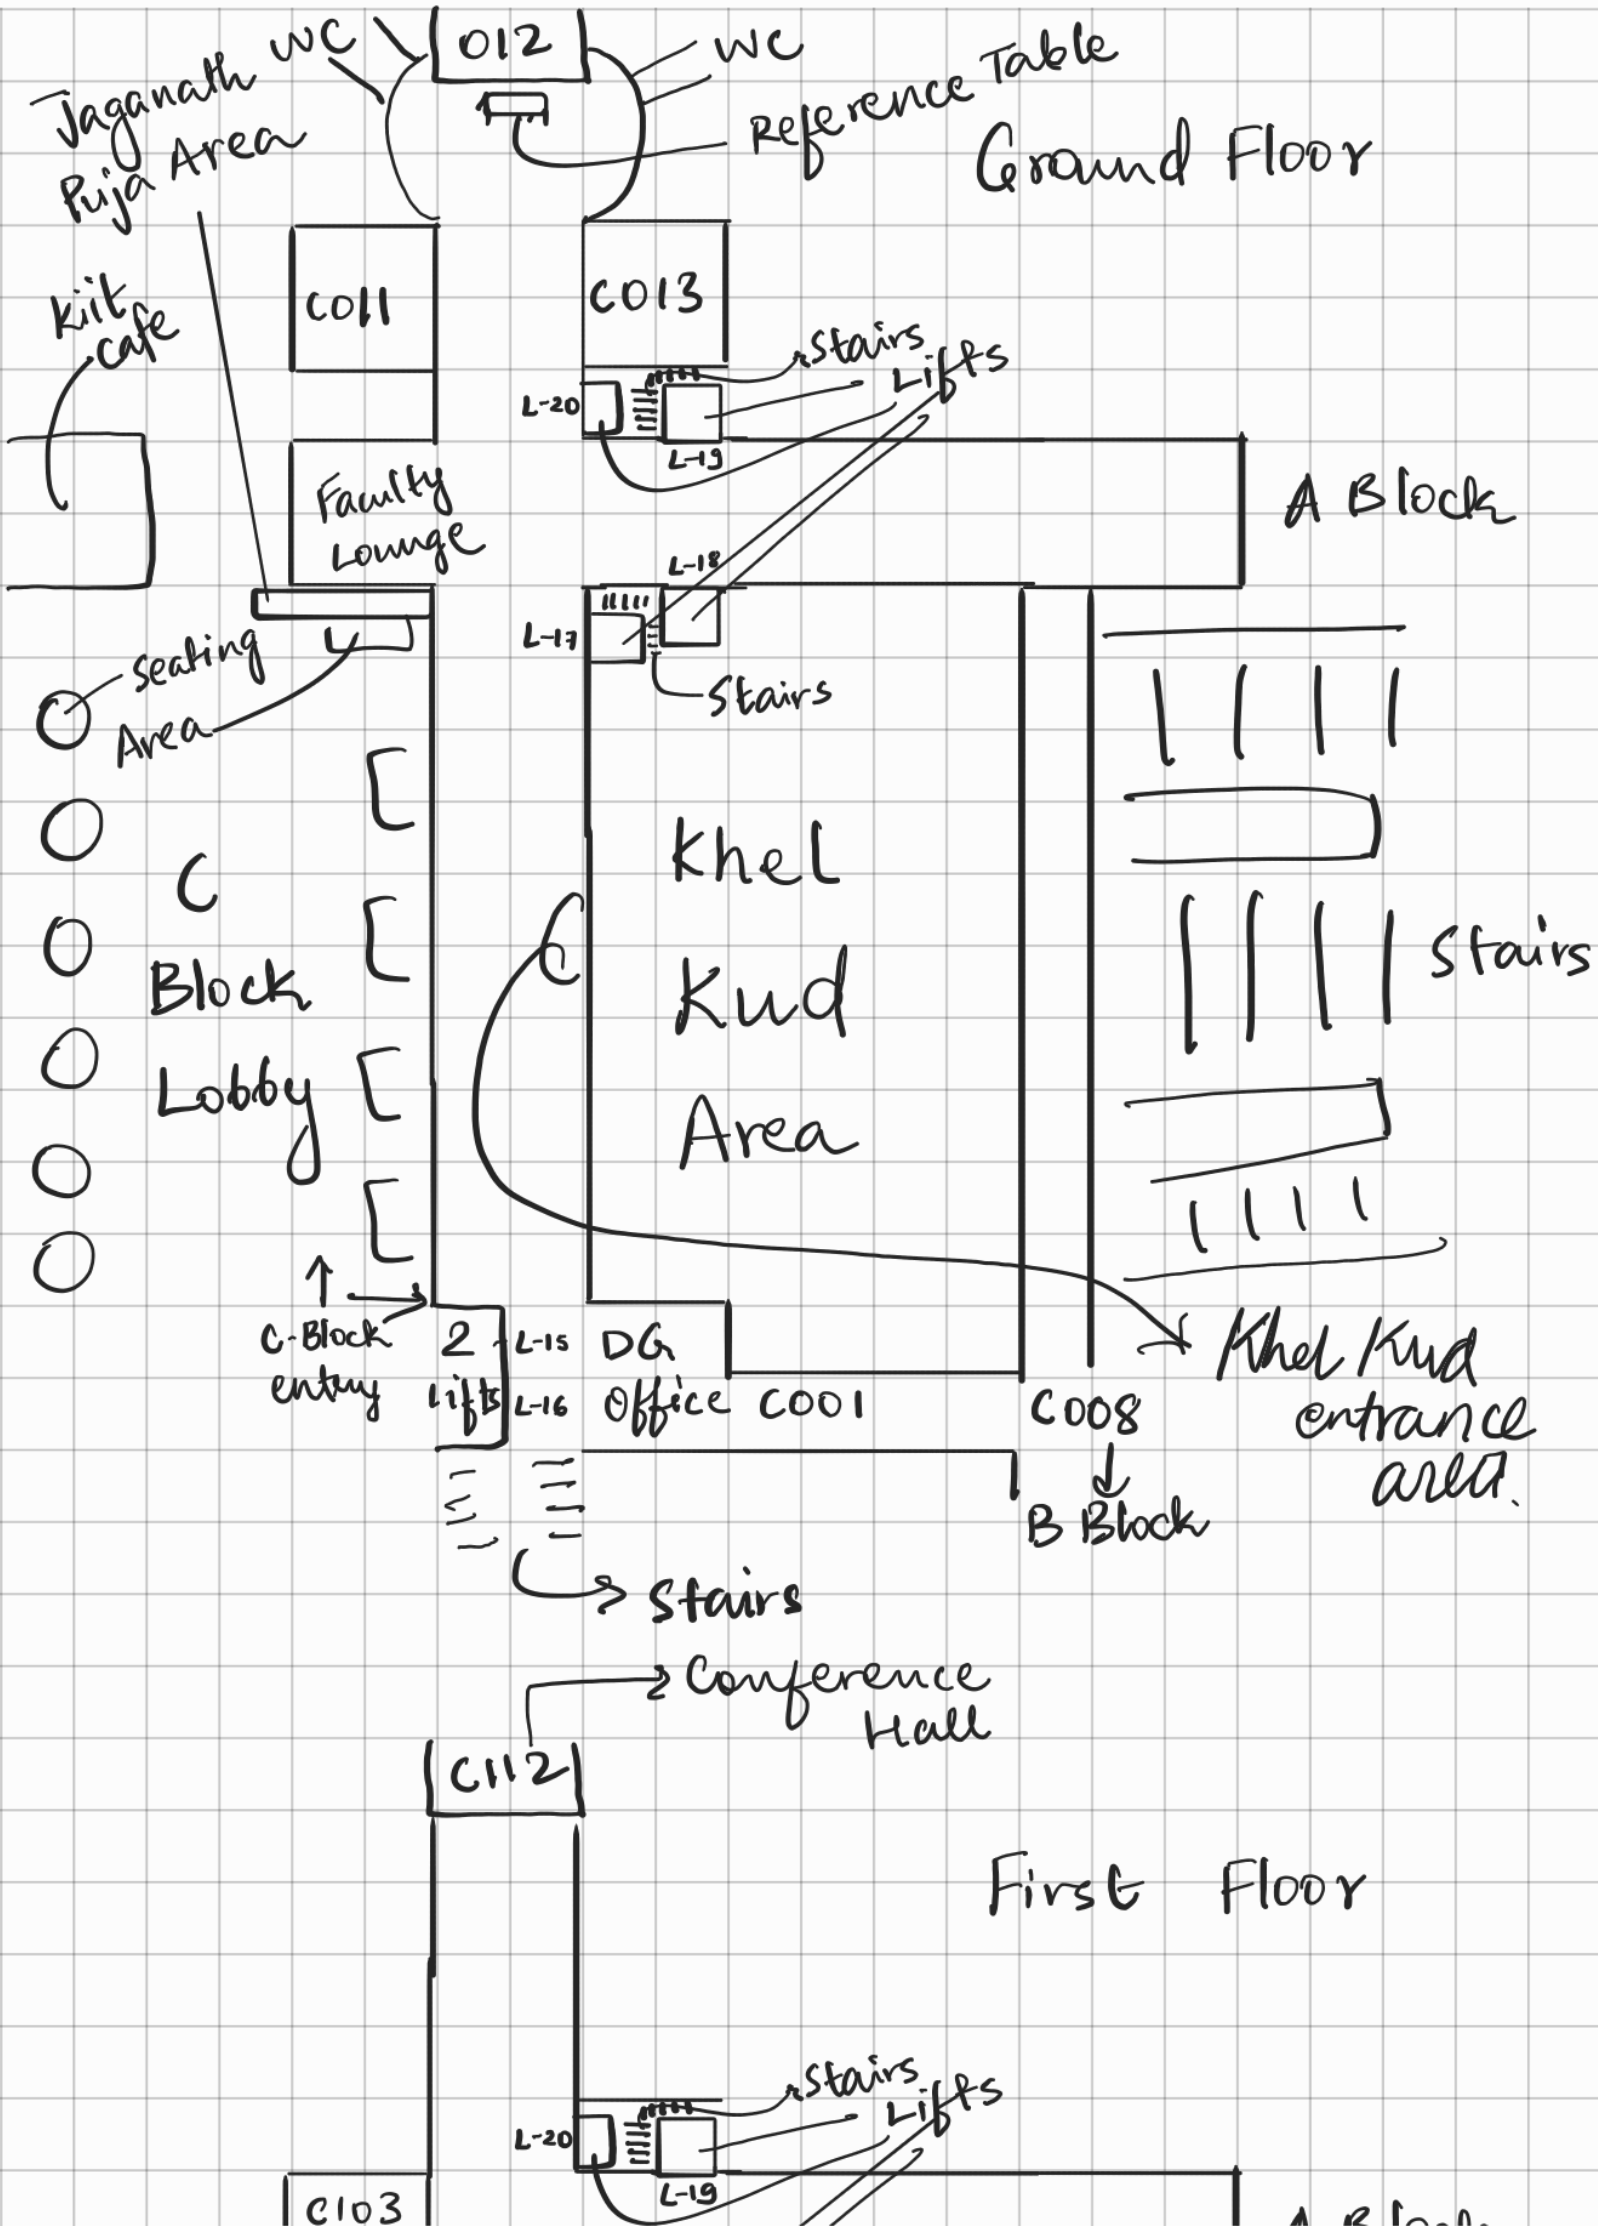
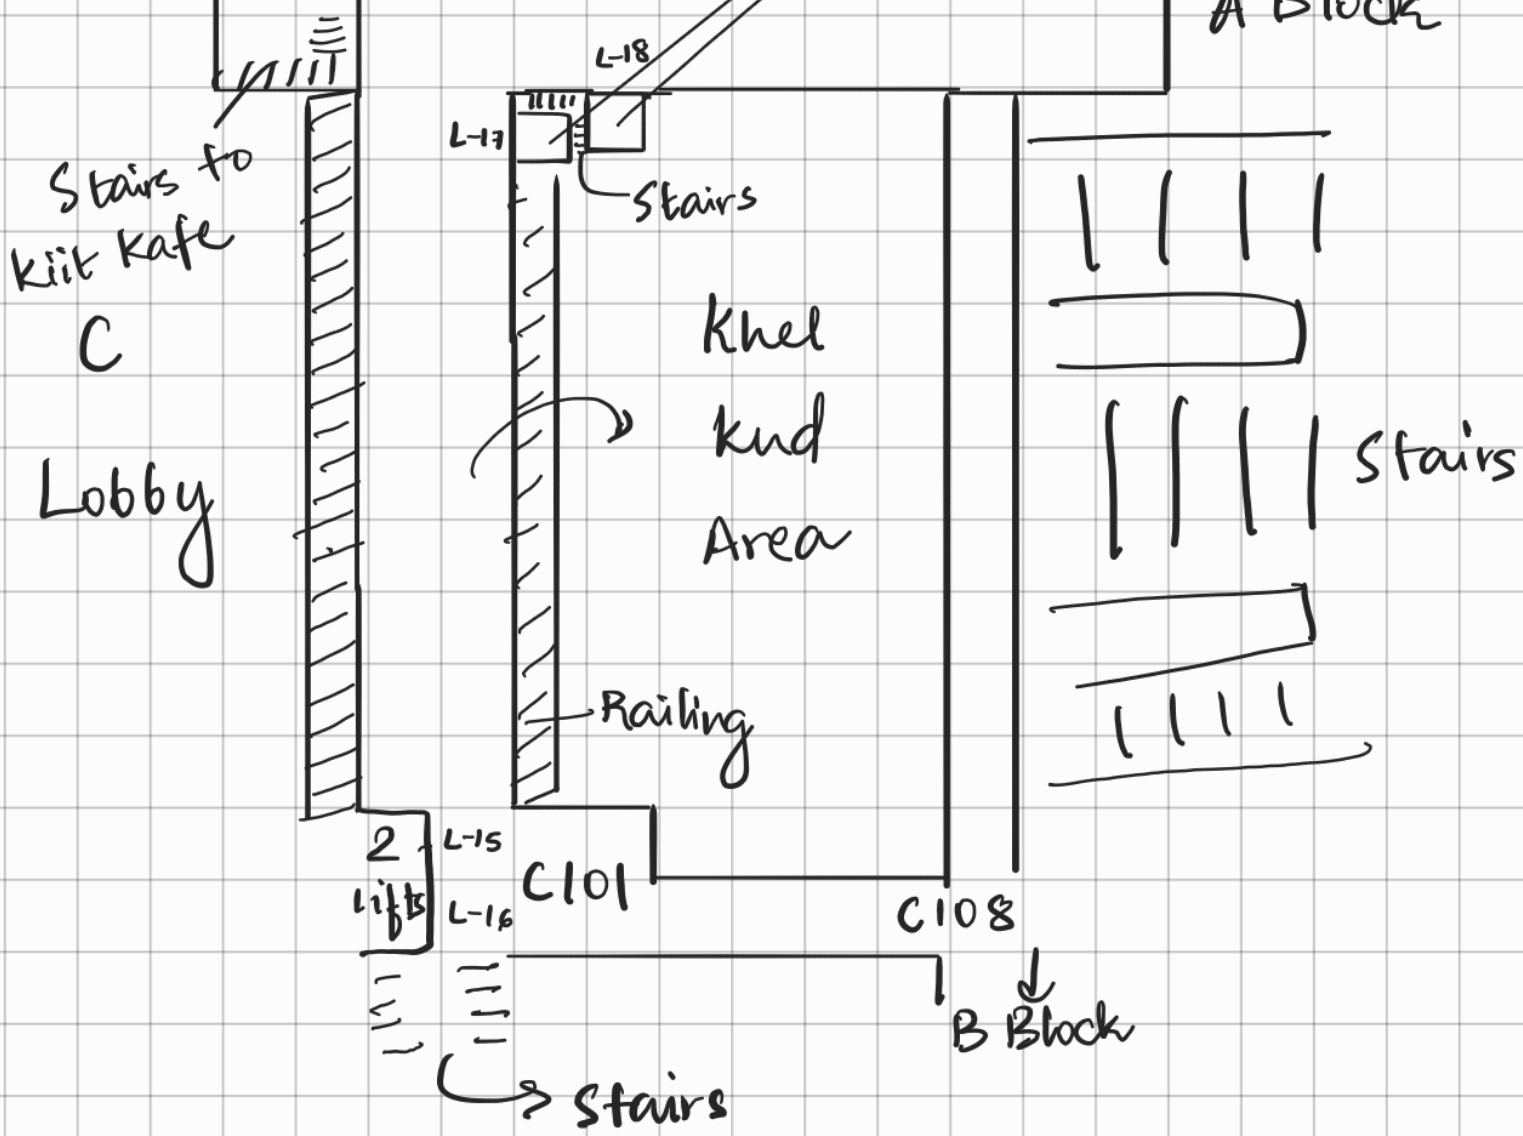
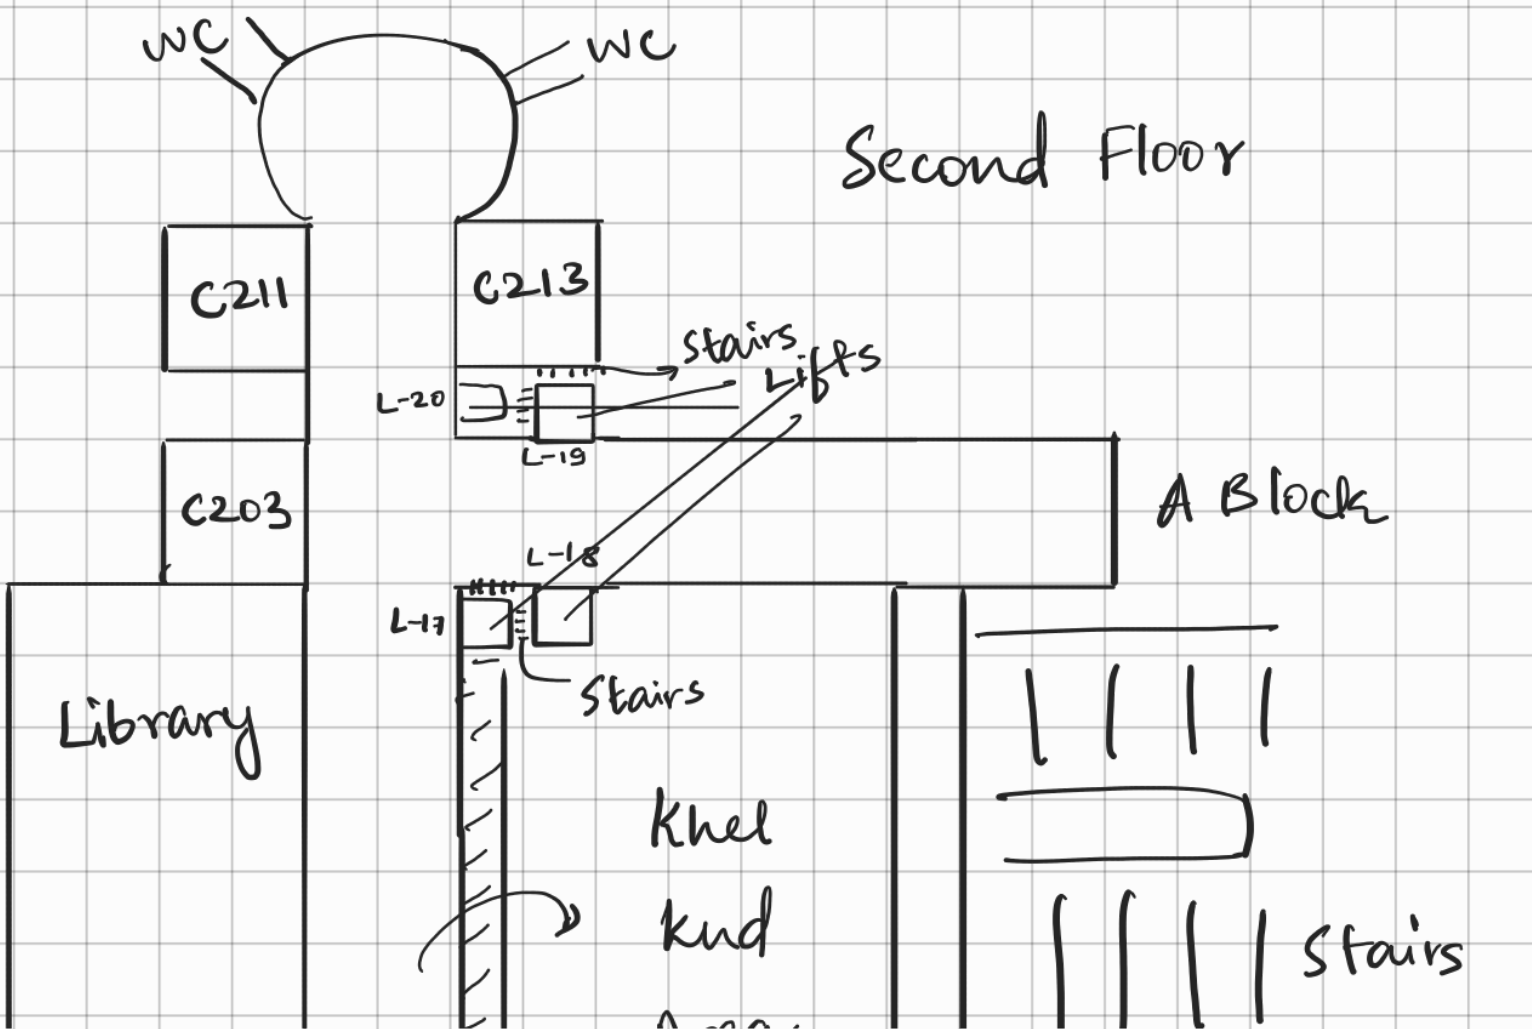
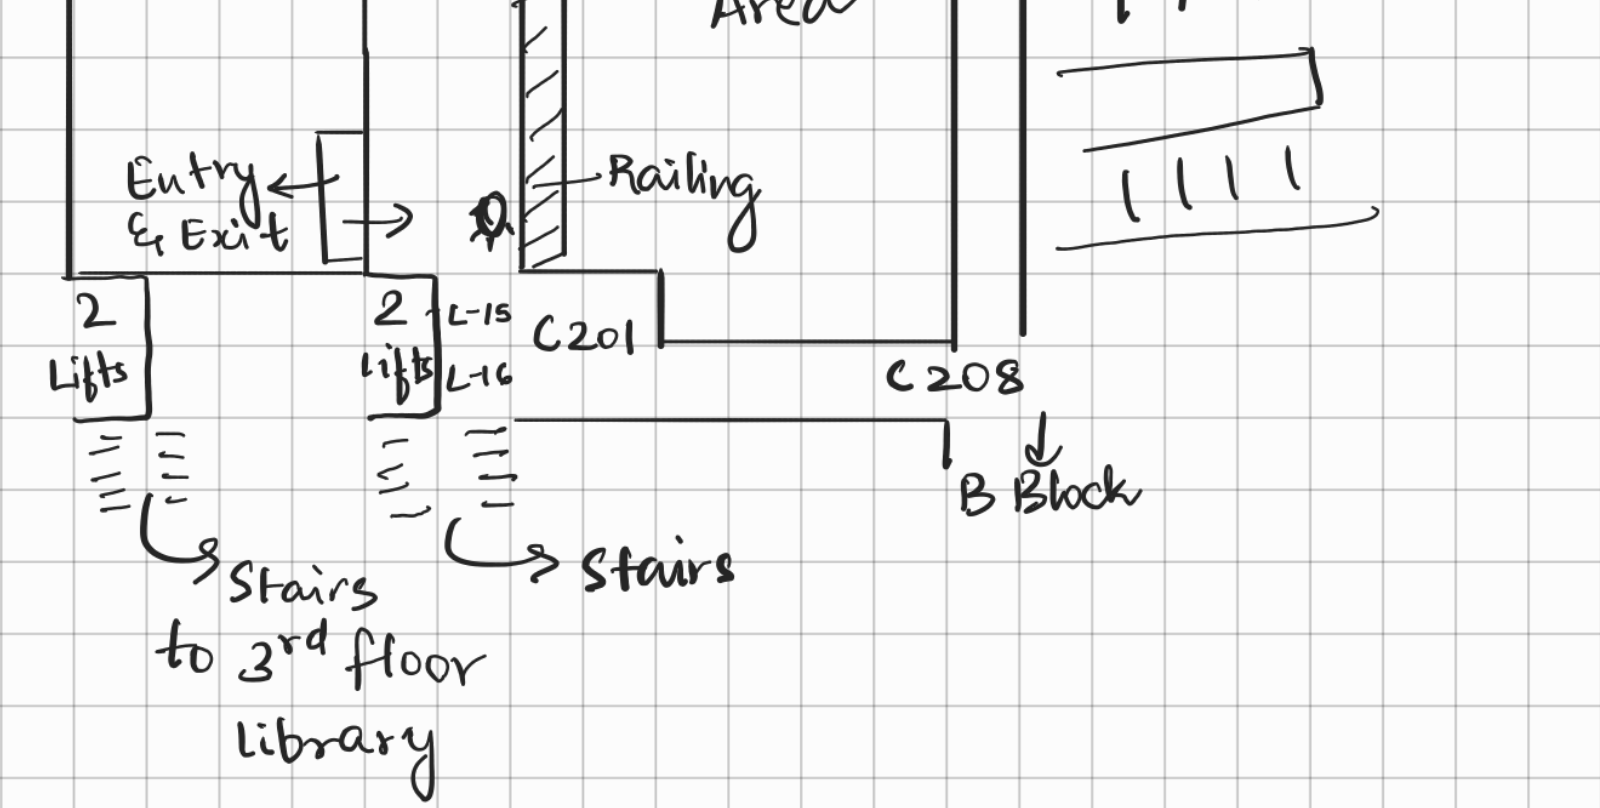
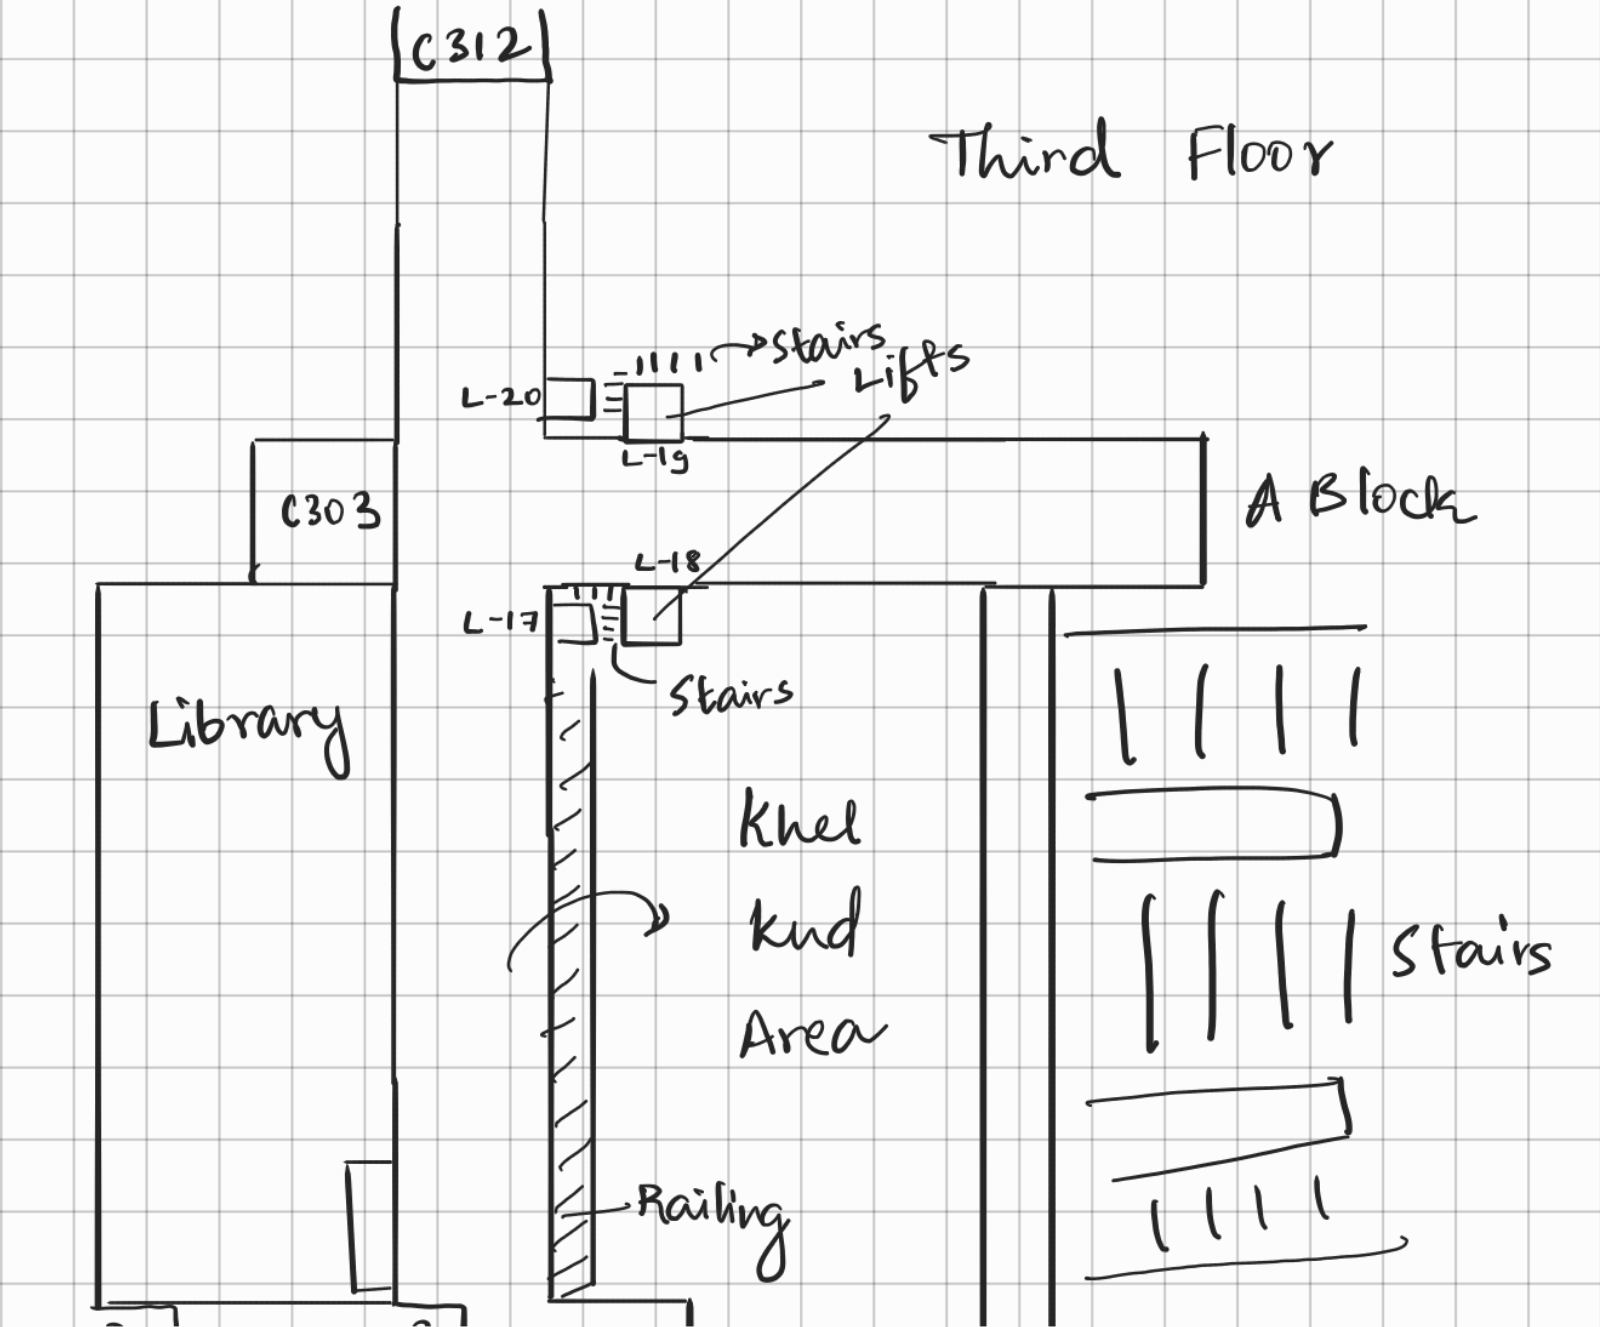
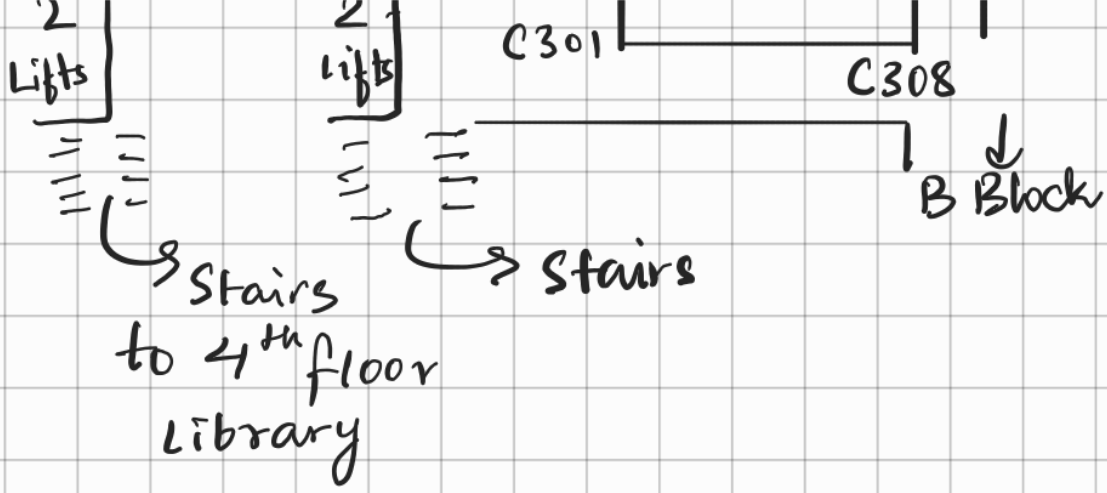

Jagannath Puja Area
WC
C12
WC
Reference Table
Ground Floor
Kiit cafe
C11
C13
Stairs
Lifts
L-20
L-19
Faculty Lounge
A Block
L-18
L-17
Stairs
Seating Area
C Block Lobby
Khel Kud Area
Stairs
C-Block entry
2 Lifts
L-15
L-16
DG Office
C001
C008
B Block
Khel Kud entrance area.
Stairs
Conference Hall
C112
First Floor
Stairs
Lifts
L-20
L-19
C103
A Block


A Block
L-18
L-17
Stairs
Stairs to kiit kafe
C
Lobby
Khel kud Area
Stairs
Railing
2 Lifts
L-15
L-16
C101
C108
B Block
Stairs


WC
WC
Second Floor
C211
C213
C203
Stairs
Lifts
L-20
L-19
A Block
L-18
L-17
Stairs
Library
Khel kud
Stairs


Area
Entry
& Exit
Railing
2
Lifts
2
Lifts
L-15
L-16
C201
C208
B Block
Stairs
to 3rd floor
Library
Stairs


C312
Third Floor
Stairs
Lifts
L-20
L-19
C303
A Block
L-18
L-17
Stairs
Library
Khel
kud
Area
Stairs
Railing


2
Lifts
2
Lifts
C301
C308
B Block
Stairs
Stairs
to 4th floor
Library